



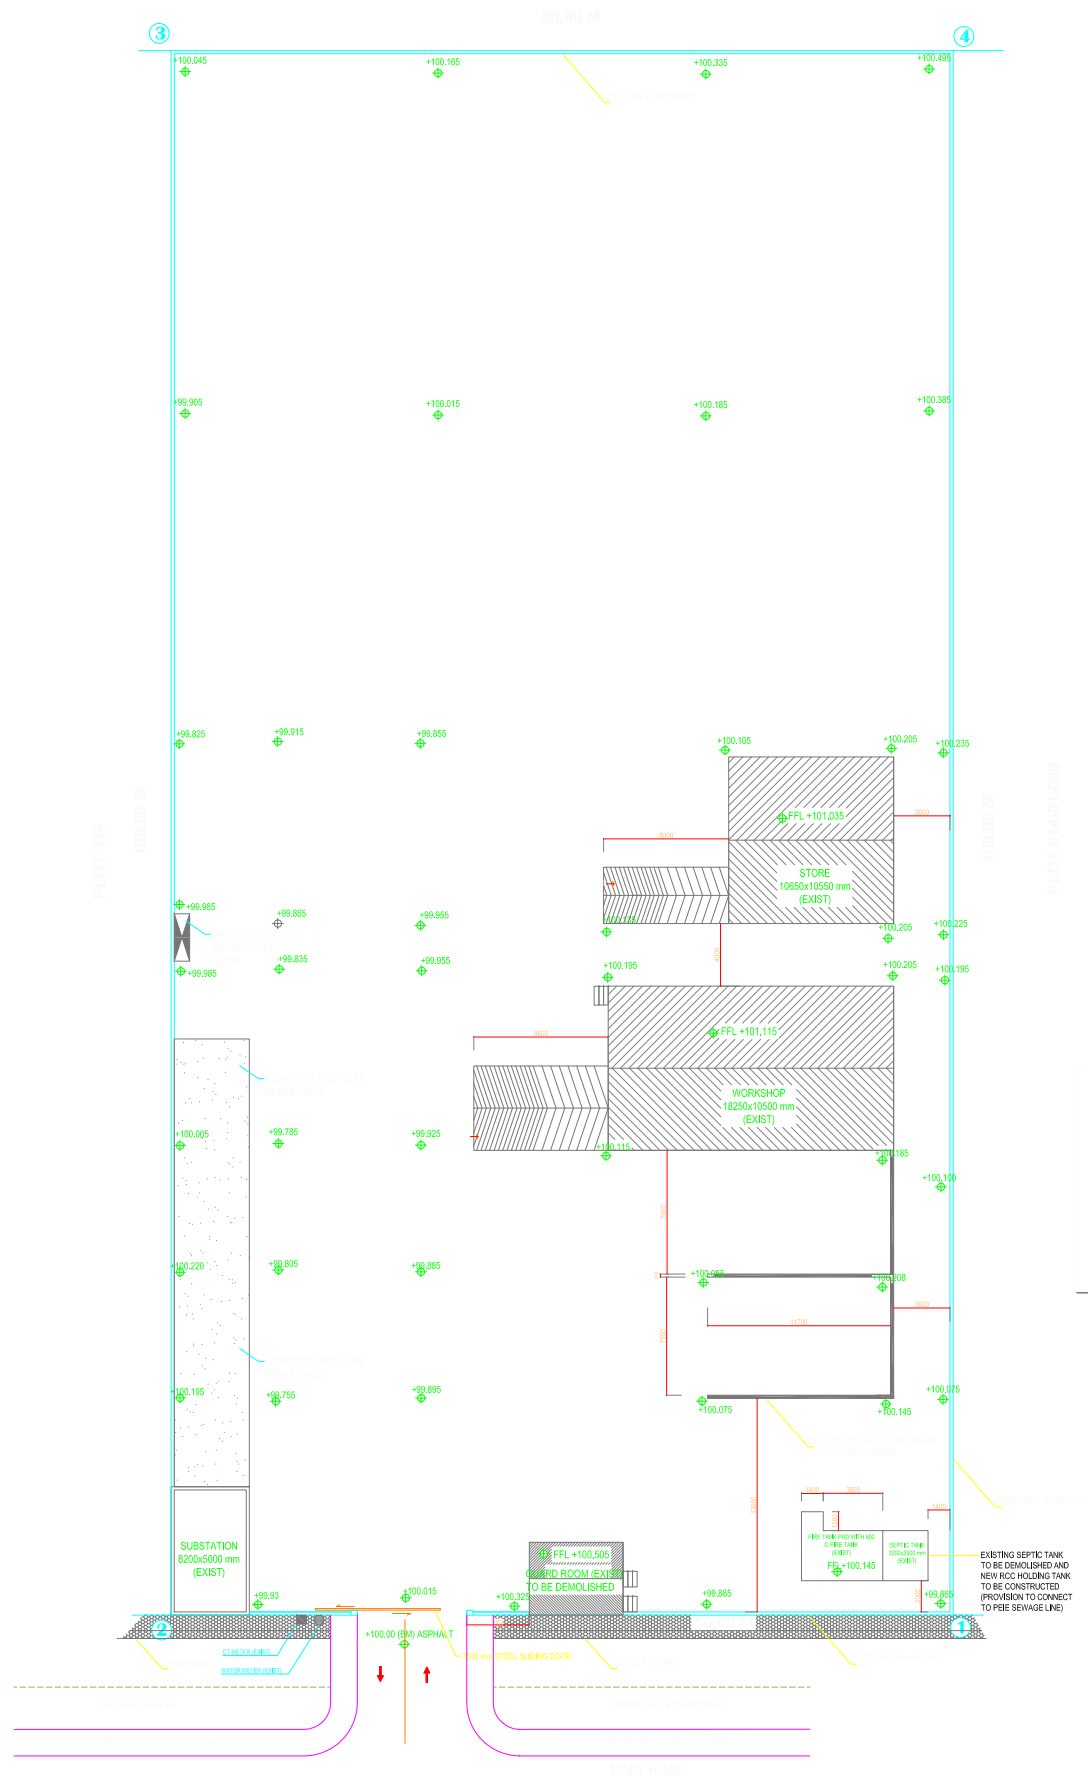

EXISTING SITE PLAN

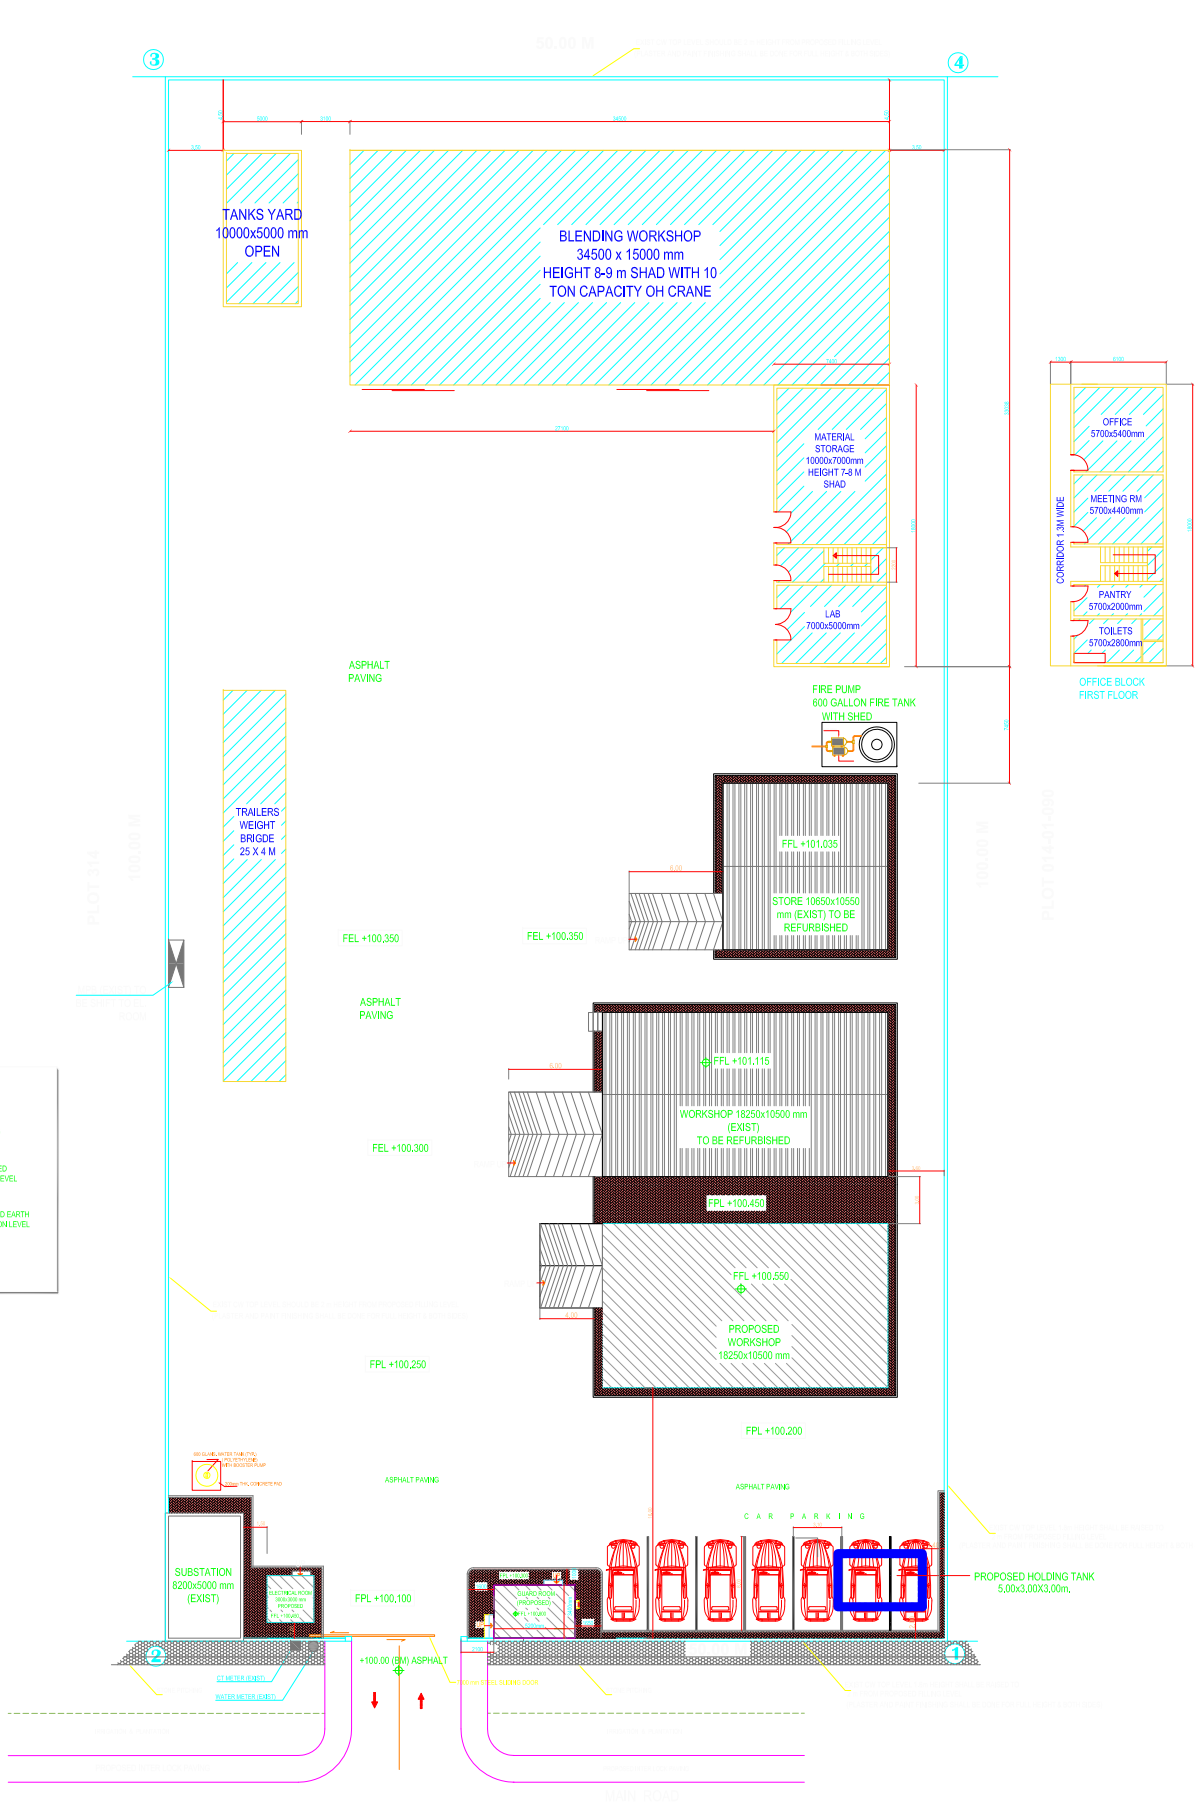

PROPOSED SITE PLAN

- NOTES:
- ALL DIMENSION ARE IN MILLIMETRES AND LEVELS IN MILLIMETRES UNLESS OTHERWISE SPECIFIED
 - ALL DIMENSIONS SHALL BE CHECKED AND VERIFIED AT SITE.
 - WRITTEN DIMENSIONS TO BE FOLLOWED, NO DIMENSION TO BE SCALED FROM THE DRAWING.
 - ALL DRAWINGS ARE INTER-RELATED AND SHALL BE READ IN CONJUNCTION WITH OTHER DRAWINGS
 - ANY DISCREPANCY FOUND IN THE DRAWING IS TO BE IMMEDIATELY BROUGHT TO THE NOTICE OF AND CLARIFIED WITH THE ENGINEER OR HIS REPRESENTATIVE AT THE SITE BEFORE COMMENCEMENT OF THE WORK OR RELATED ITEMS OF WORK.

AREA STATEMENTS

PLOT AREA	= 5000.00 SQ.MTS.
PROPOSED CHEMICAL STORE	= 191.625 M ²
EXIST CHEMICAL STORE	= 191.625 M ²
STORAGE	= 112.357 M ²
GUARD ROOM	= 17.68 M ²
ELECTRICAL ROOM	= 9.00 M ²
TOTAL AREA	= 522.87 M ²

ADDITIONAL SHADED AREA	
BLENDING WORKSHOP	= 517.50 M ²
STORAGE & LAB	= 133.20 M ²
OFFICES	= 133.20 M ²

NO:	DATE	REVISION	BY:	APP:



CONSTRUCTION OF MAINTENANCE WORKSHOP
AT NIZWA INDUSTRIAL ESTATE

SITE PLAN
(EXISTING AND PROPOSAL)

CAD:	JOHNSON	JOB NO:	PROJECT NO:
CHECKED:	FAWAZ	SCALE:	1:350
APPROVED:	SALIM HAMED SALIM AL KANYANI	DWG. NO:	AR - 01
DATE:	JULY - 2018		